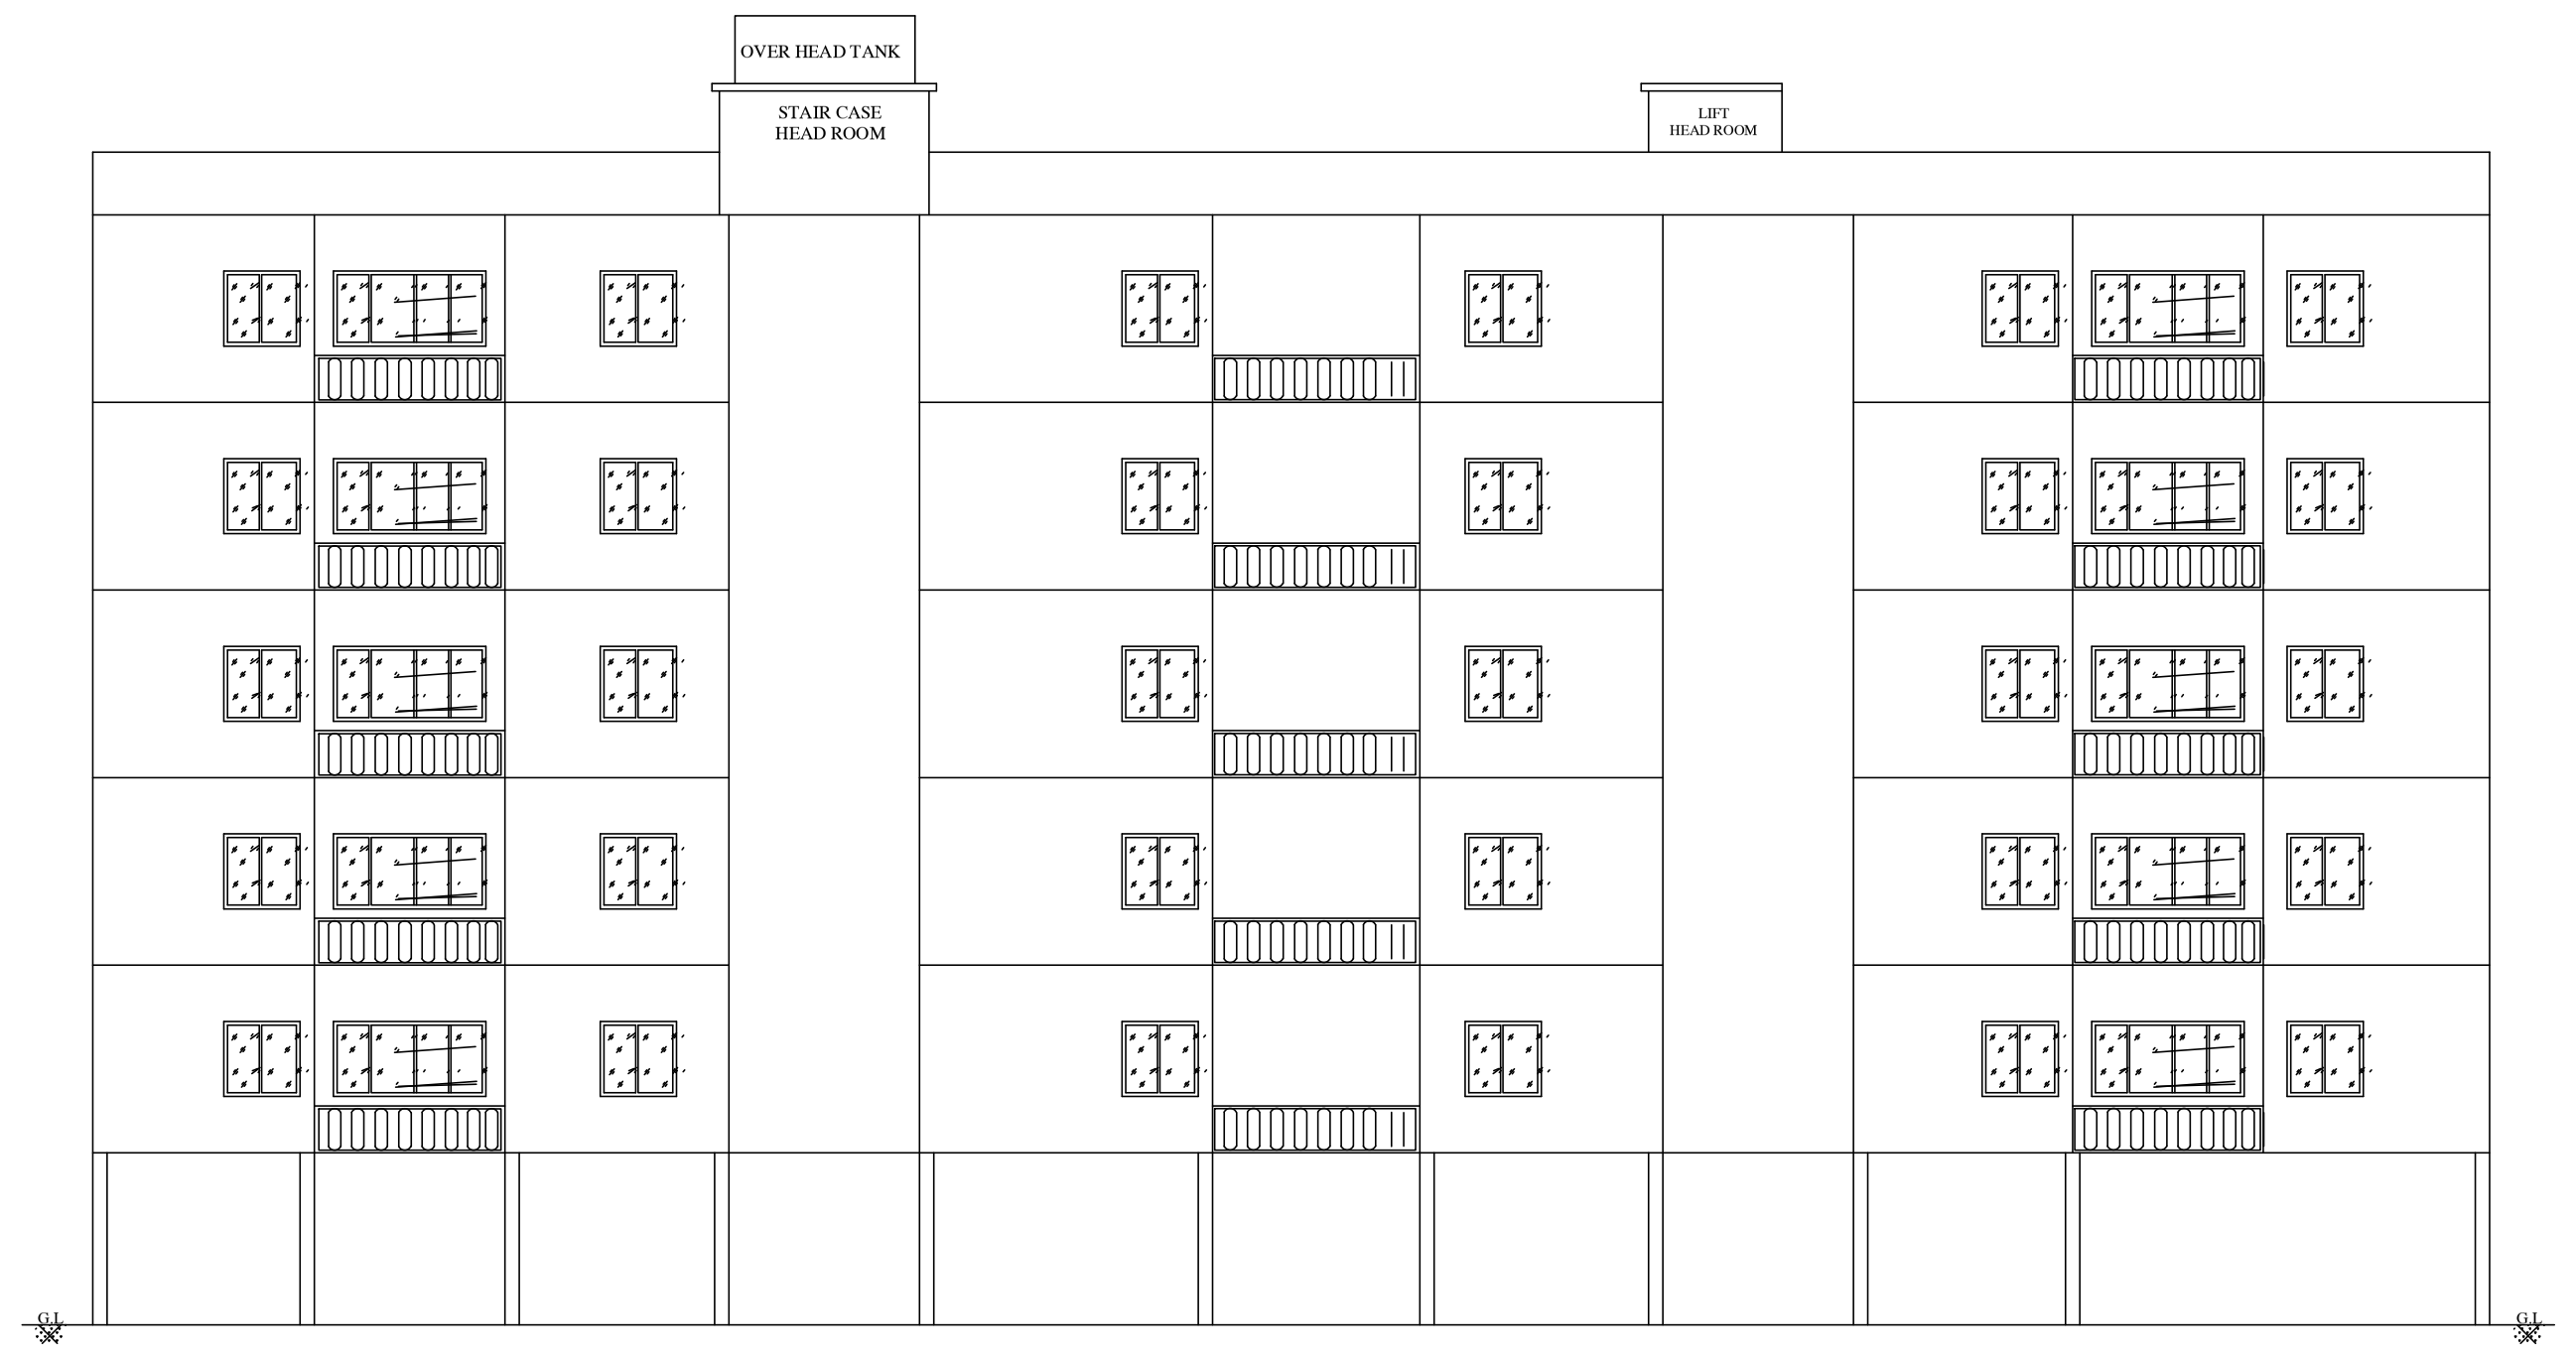

ELEVATION

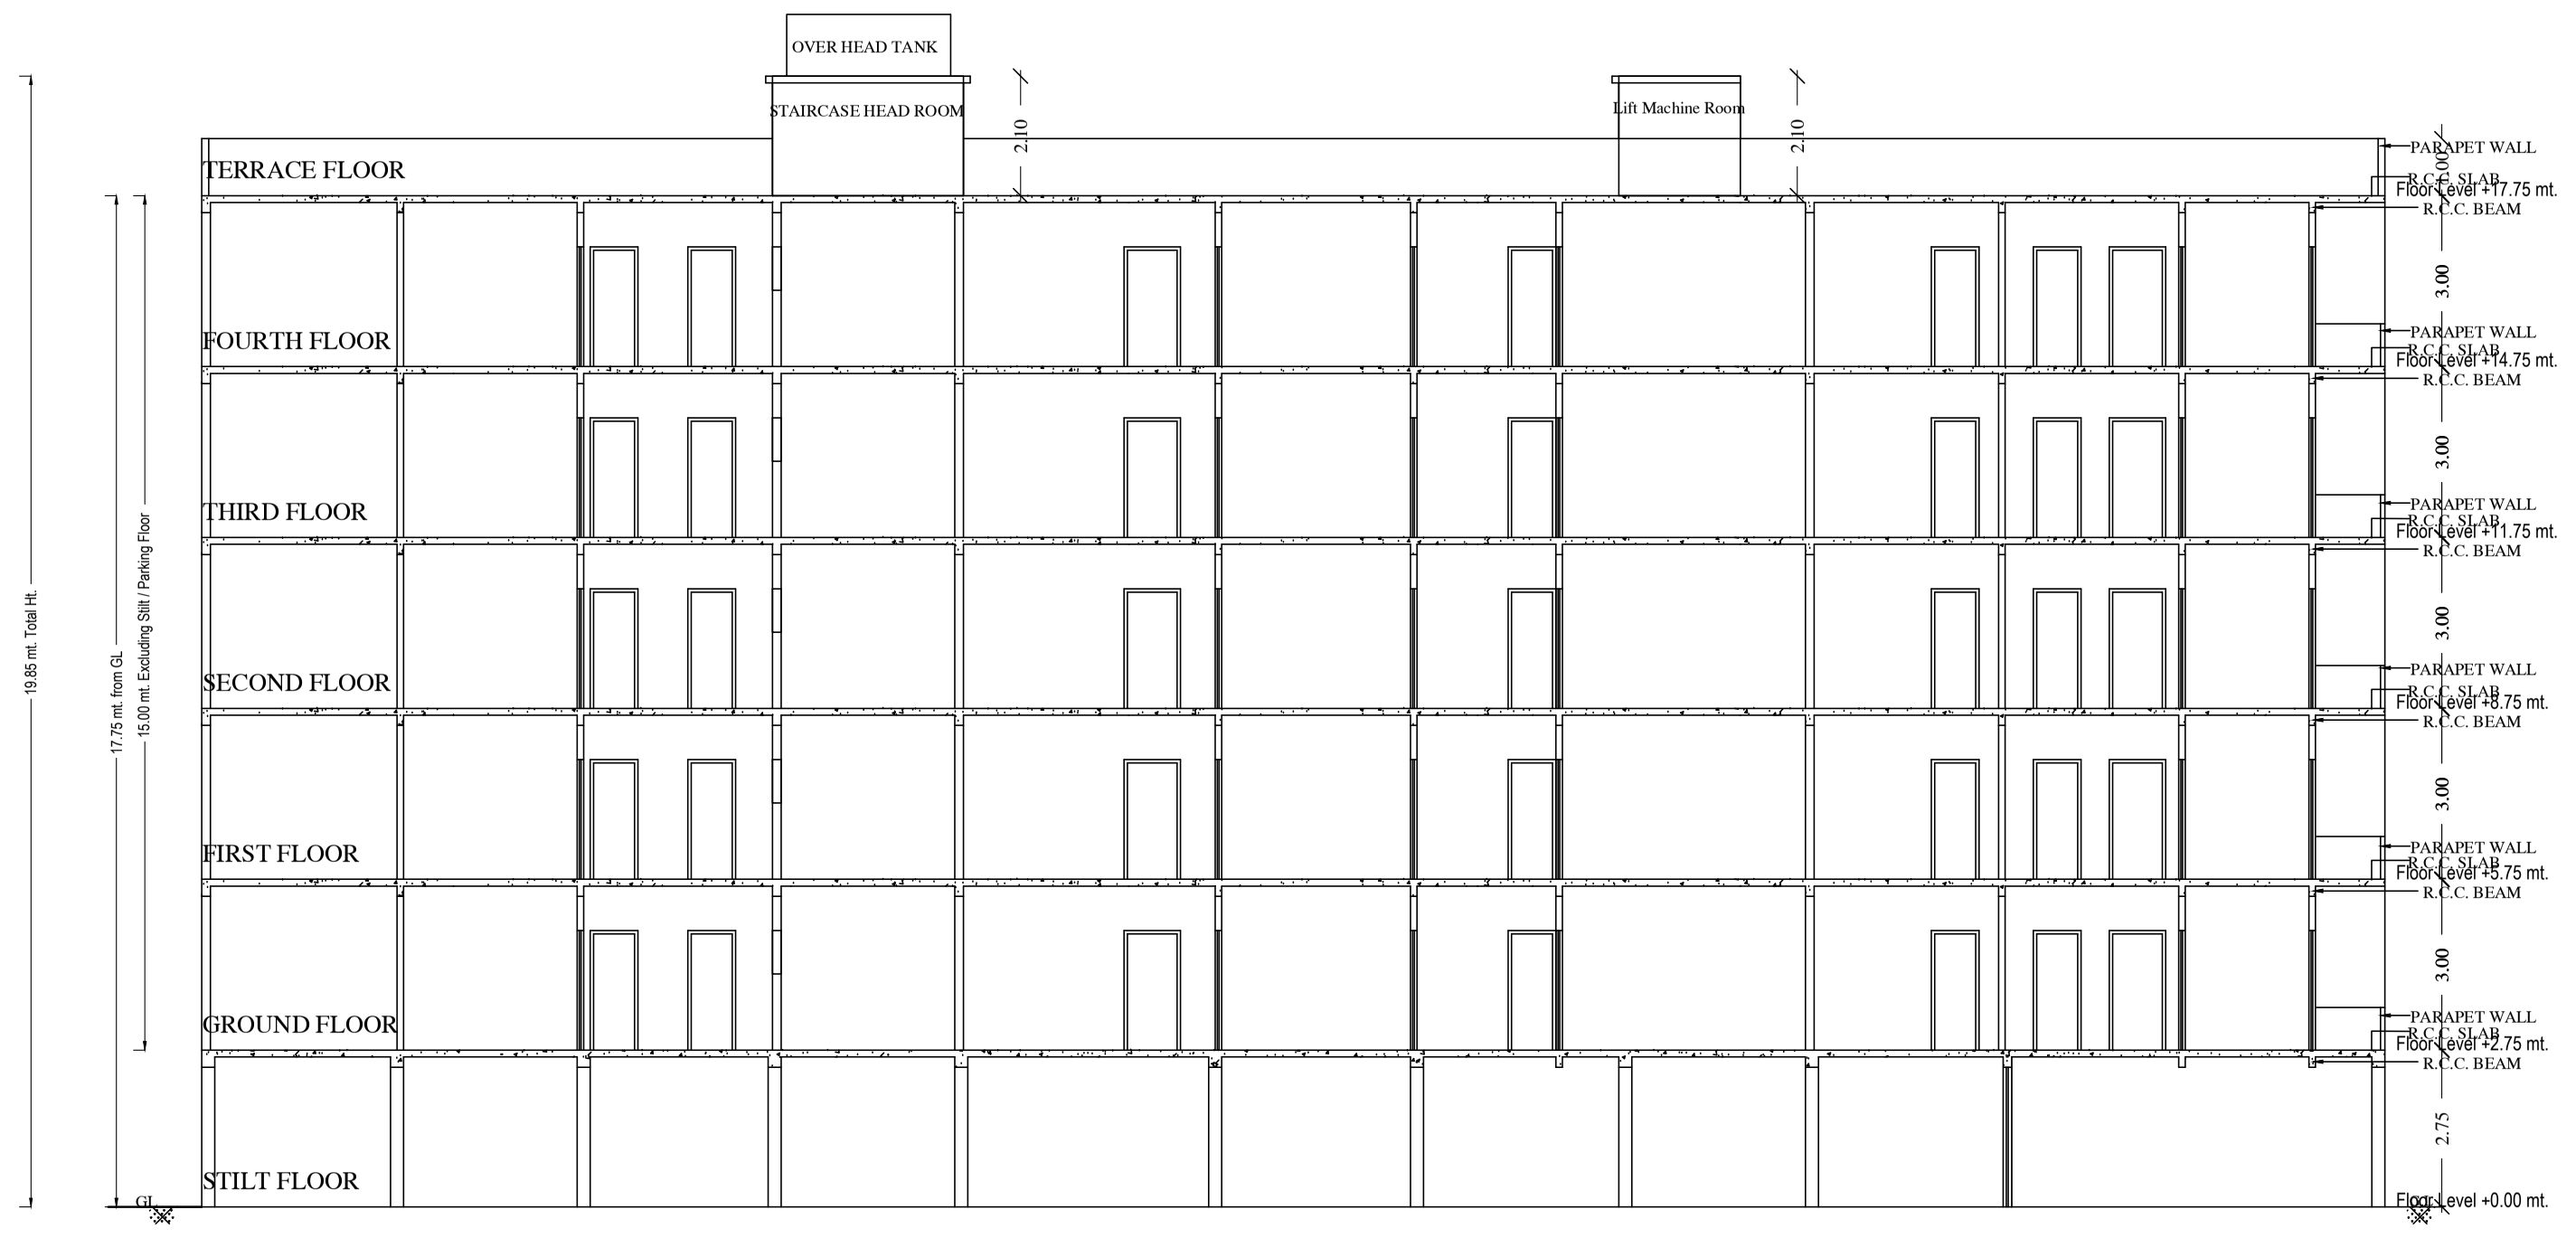

SECTION @ 'A'A'

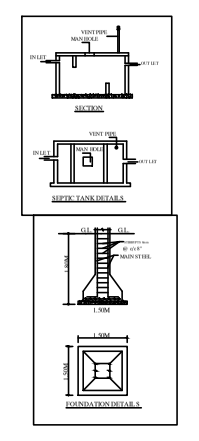

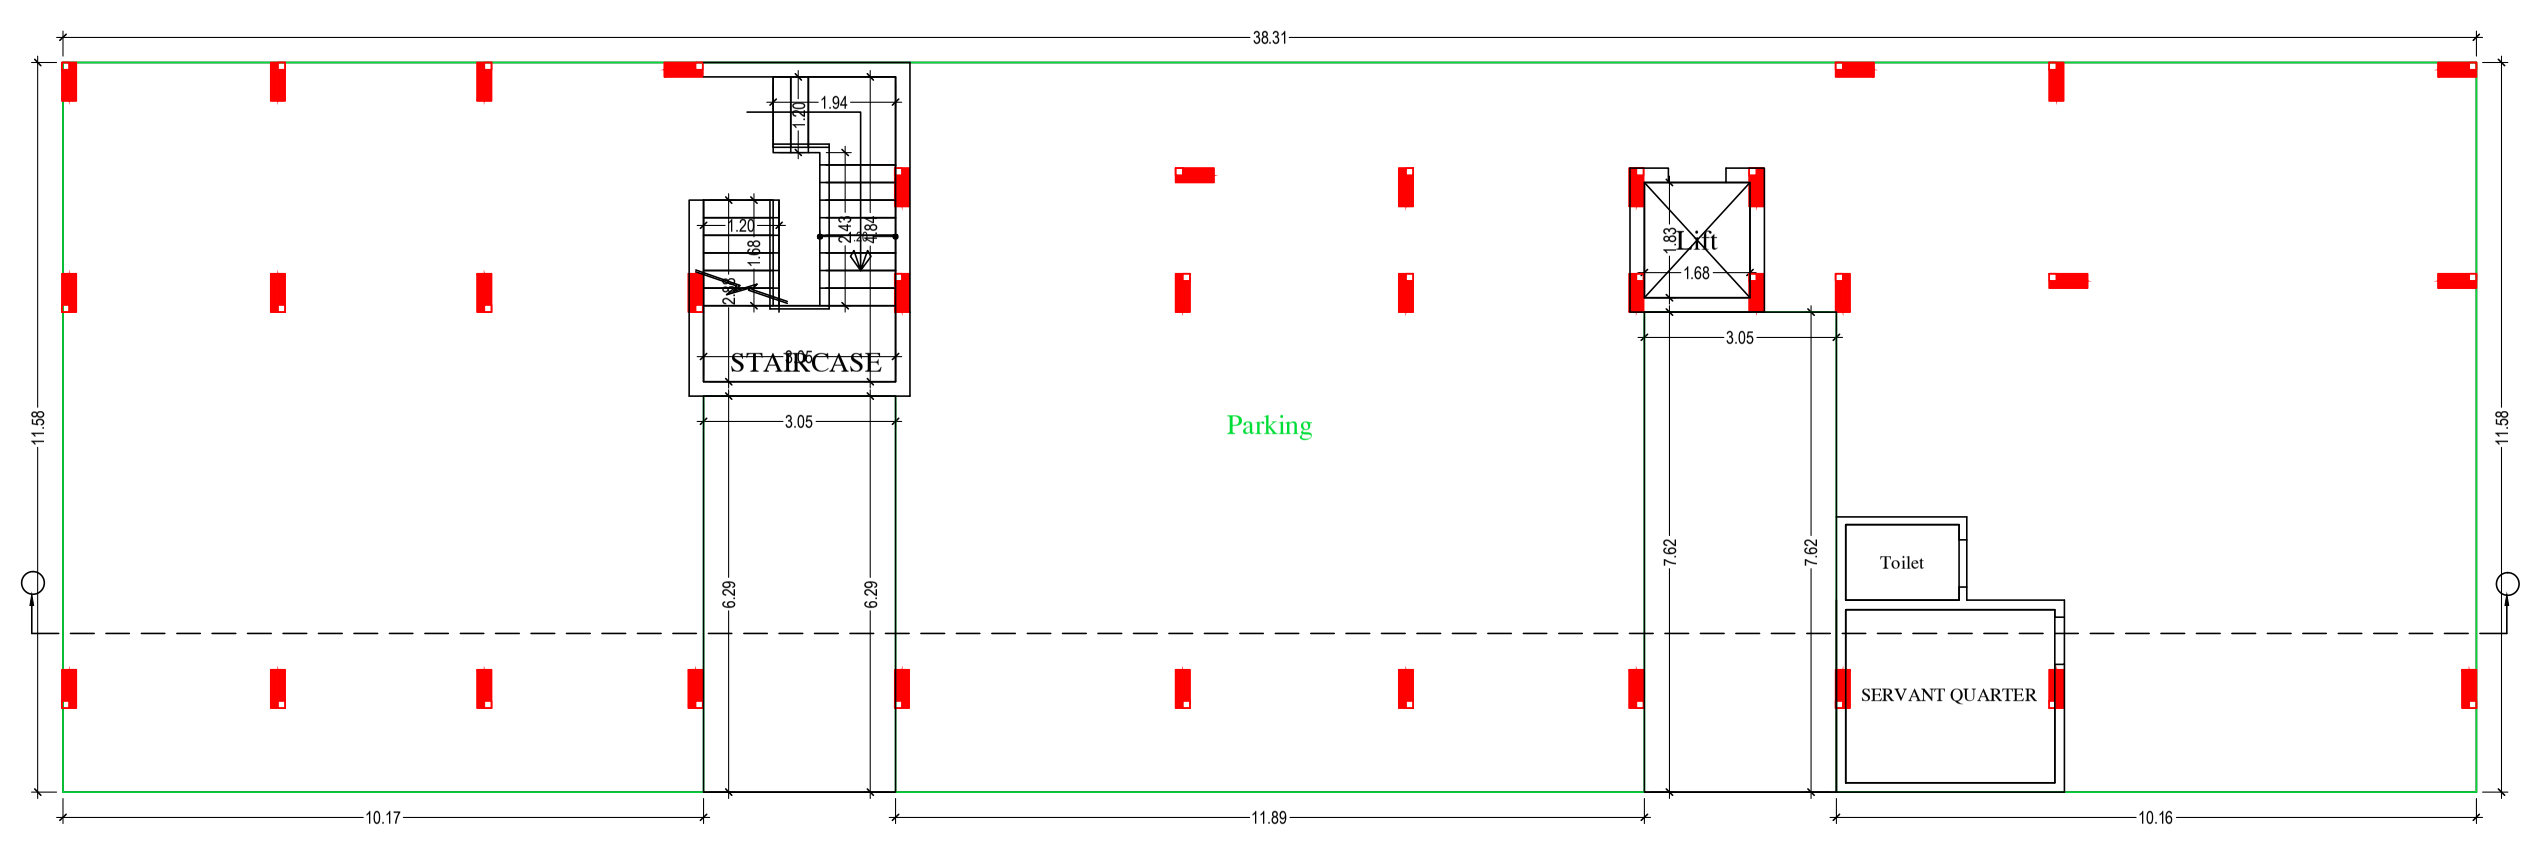

STILT FLOOR PLAN
(SCALE 1:100)

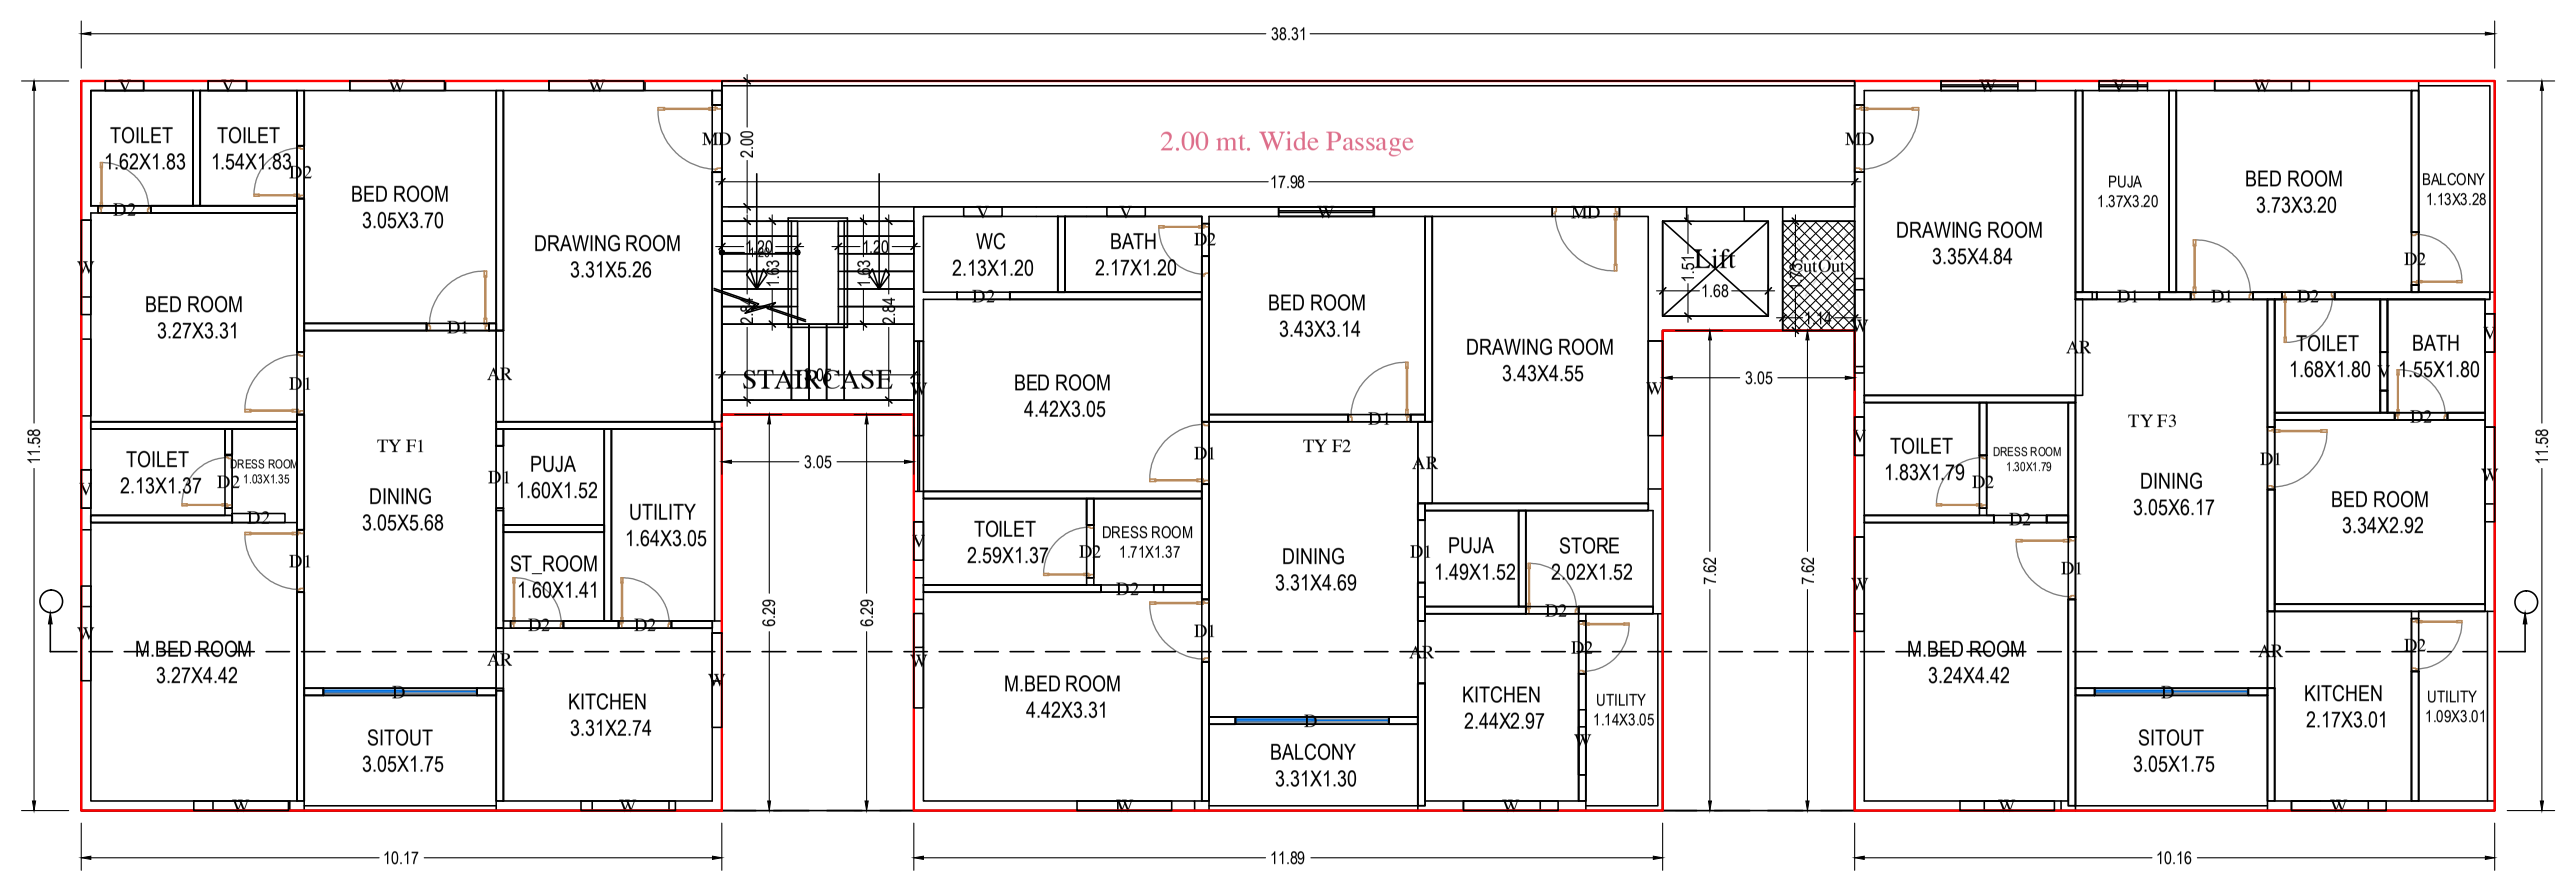

TYPICAL - GROUND, FIRST, SECOND& FOURTH FLOOR PLAN
(Proposed)
(SCALE 1:100)

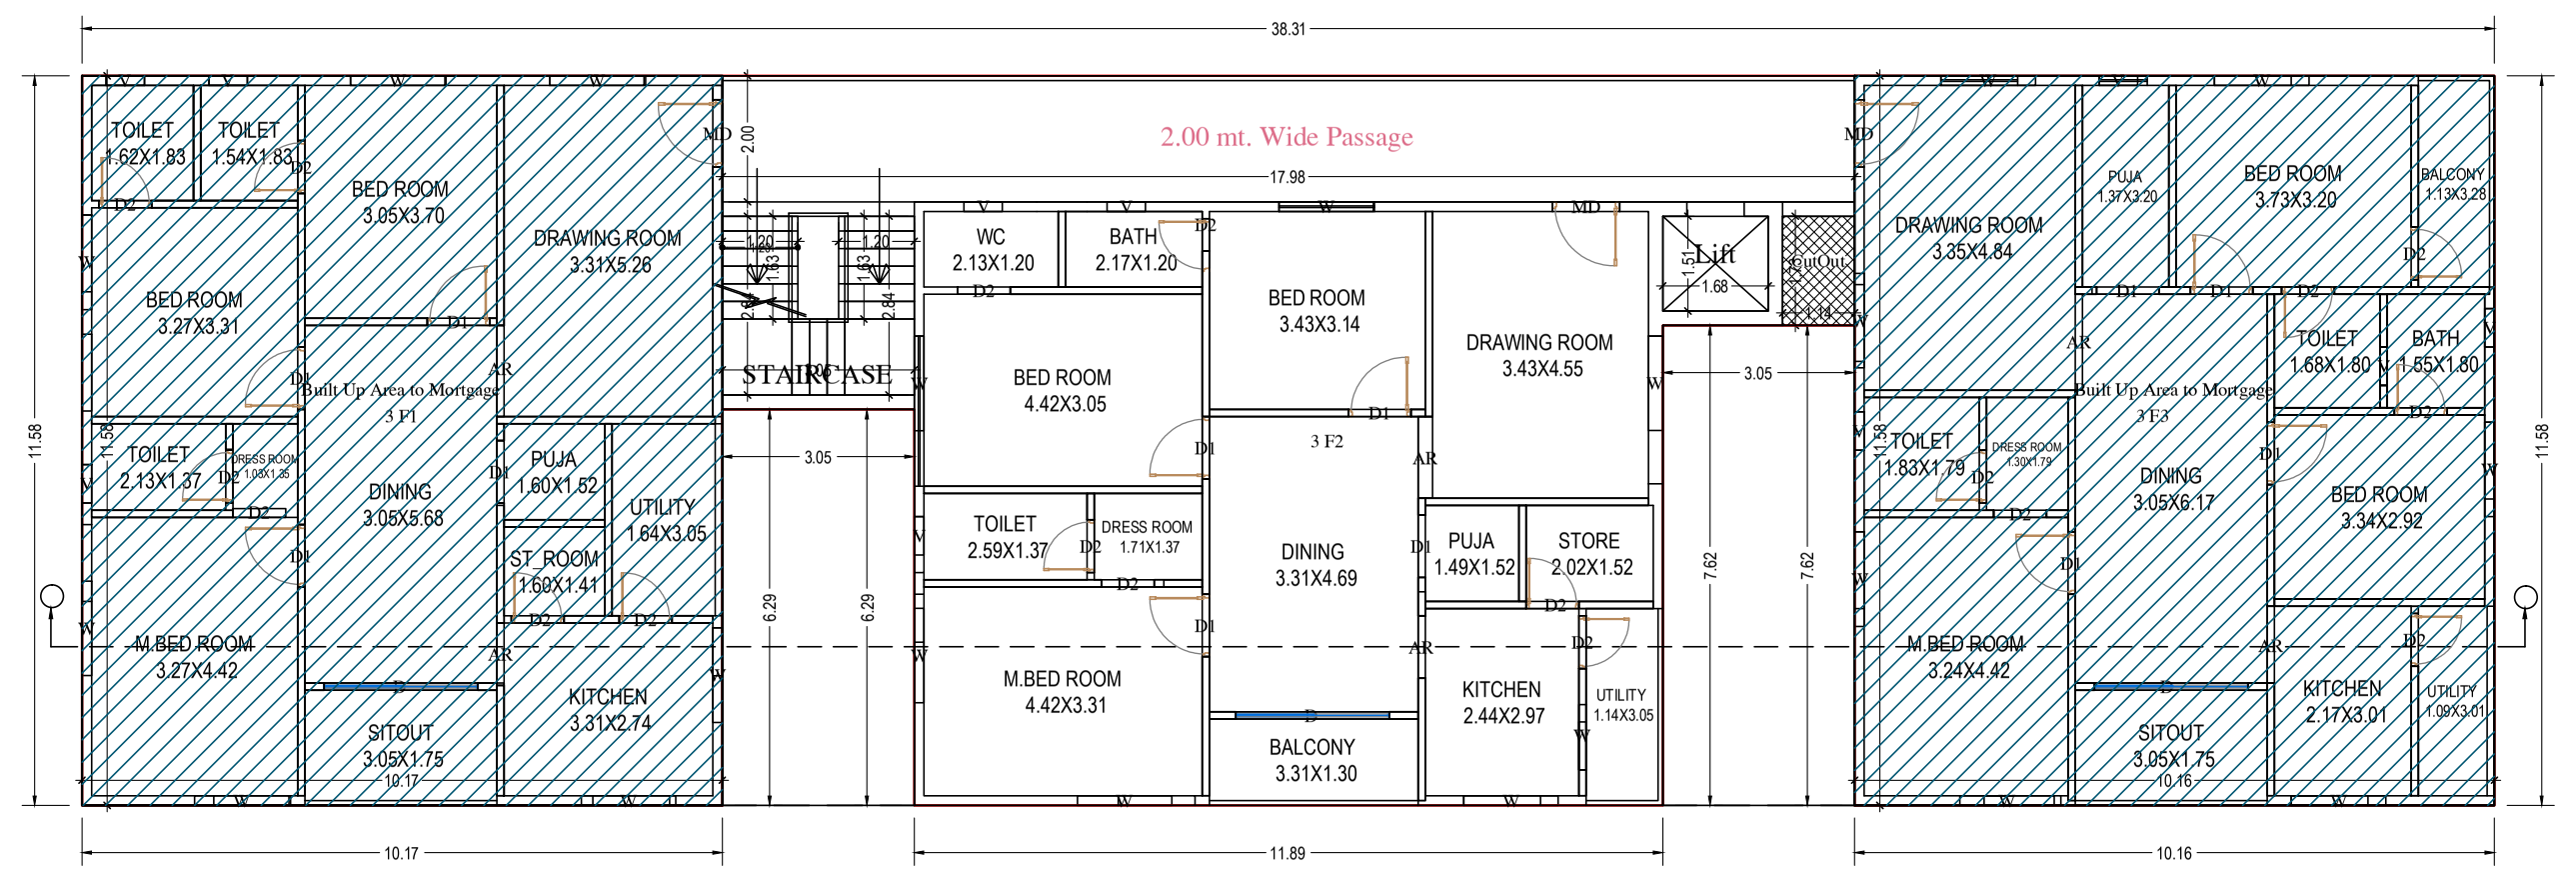

THIRD FLOOR PLAN
(Proposed)
(SCALE 1:100)

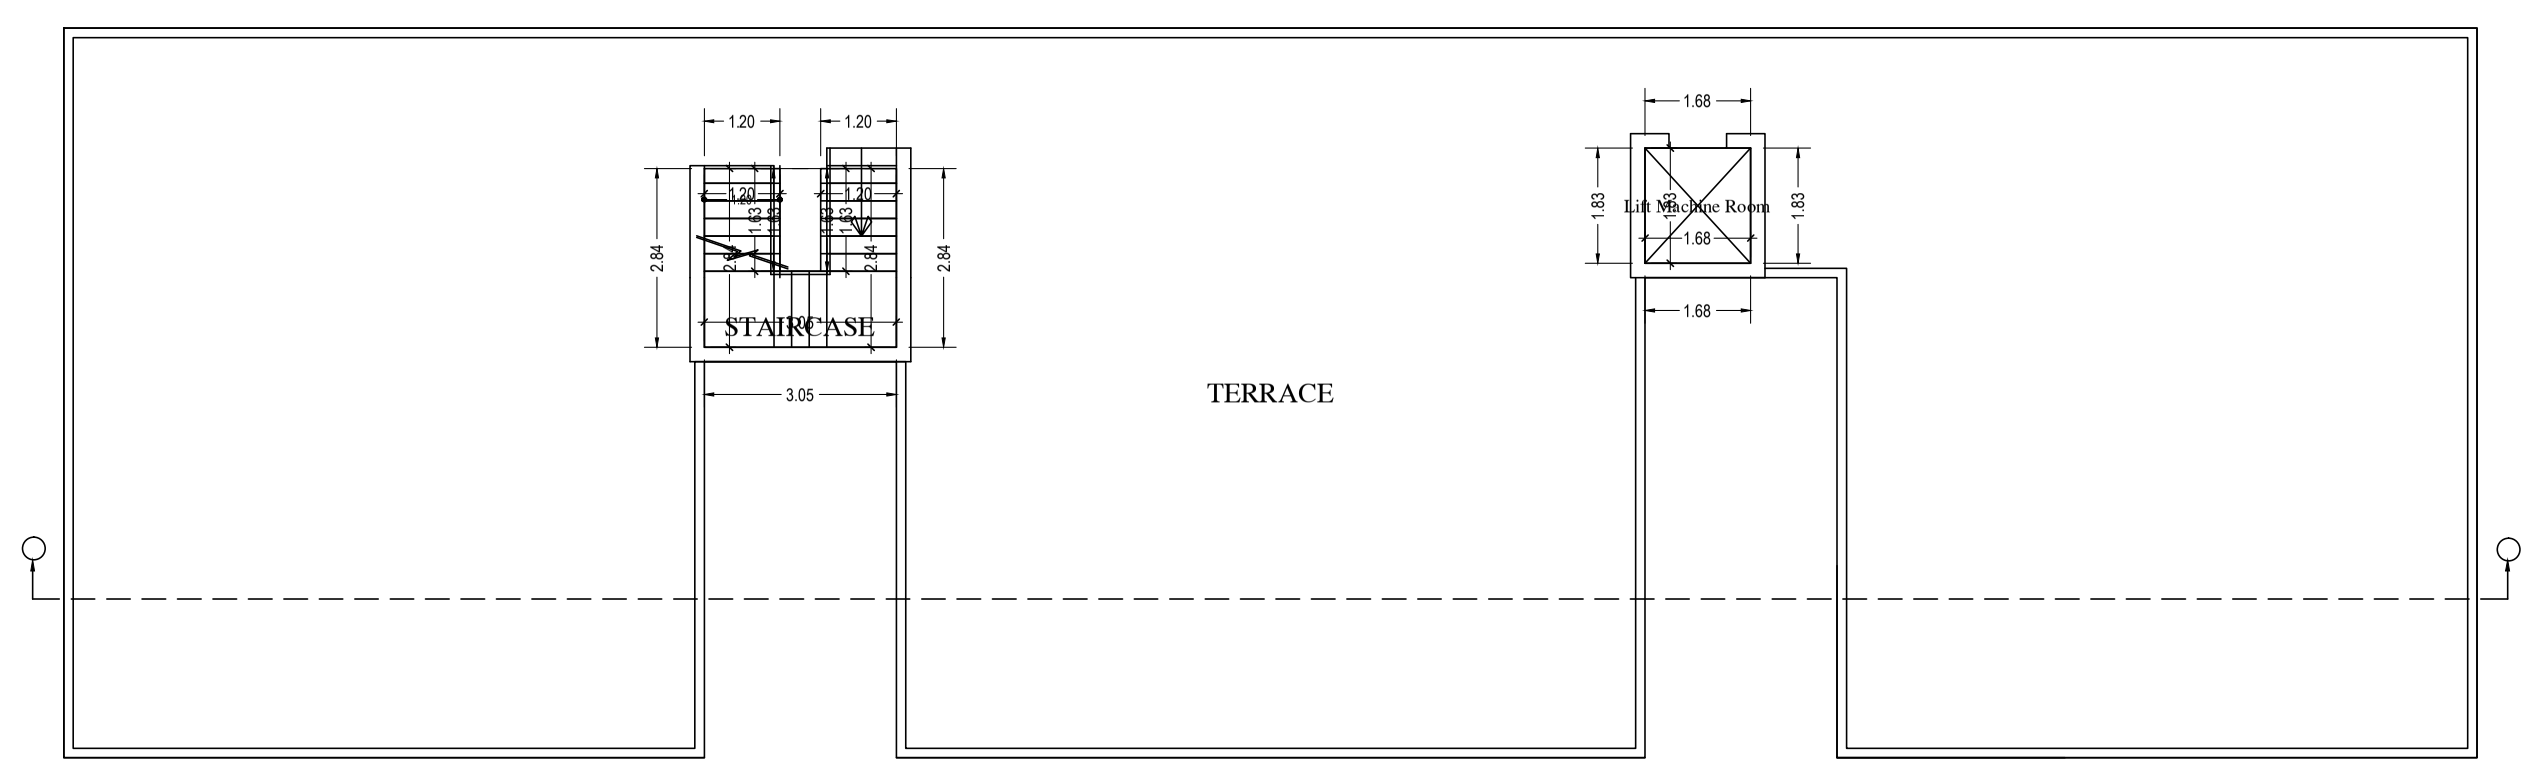

TERRACE FLOOR PLAN
(SCALE 1:100)

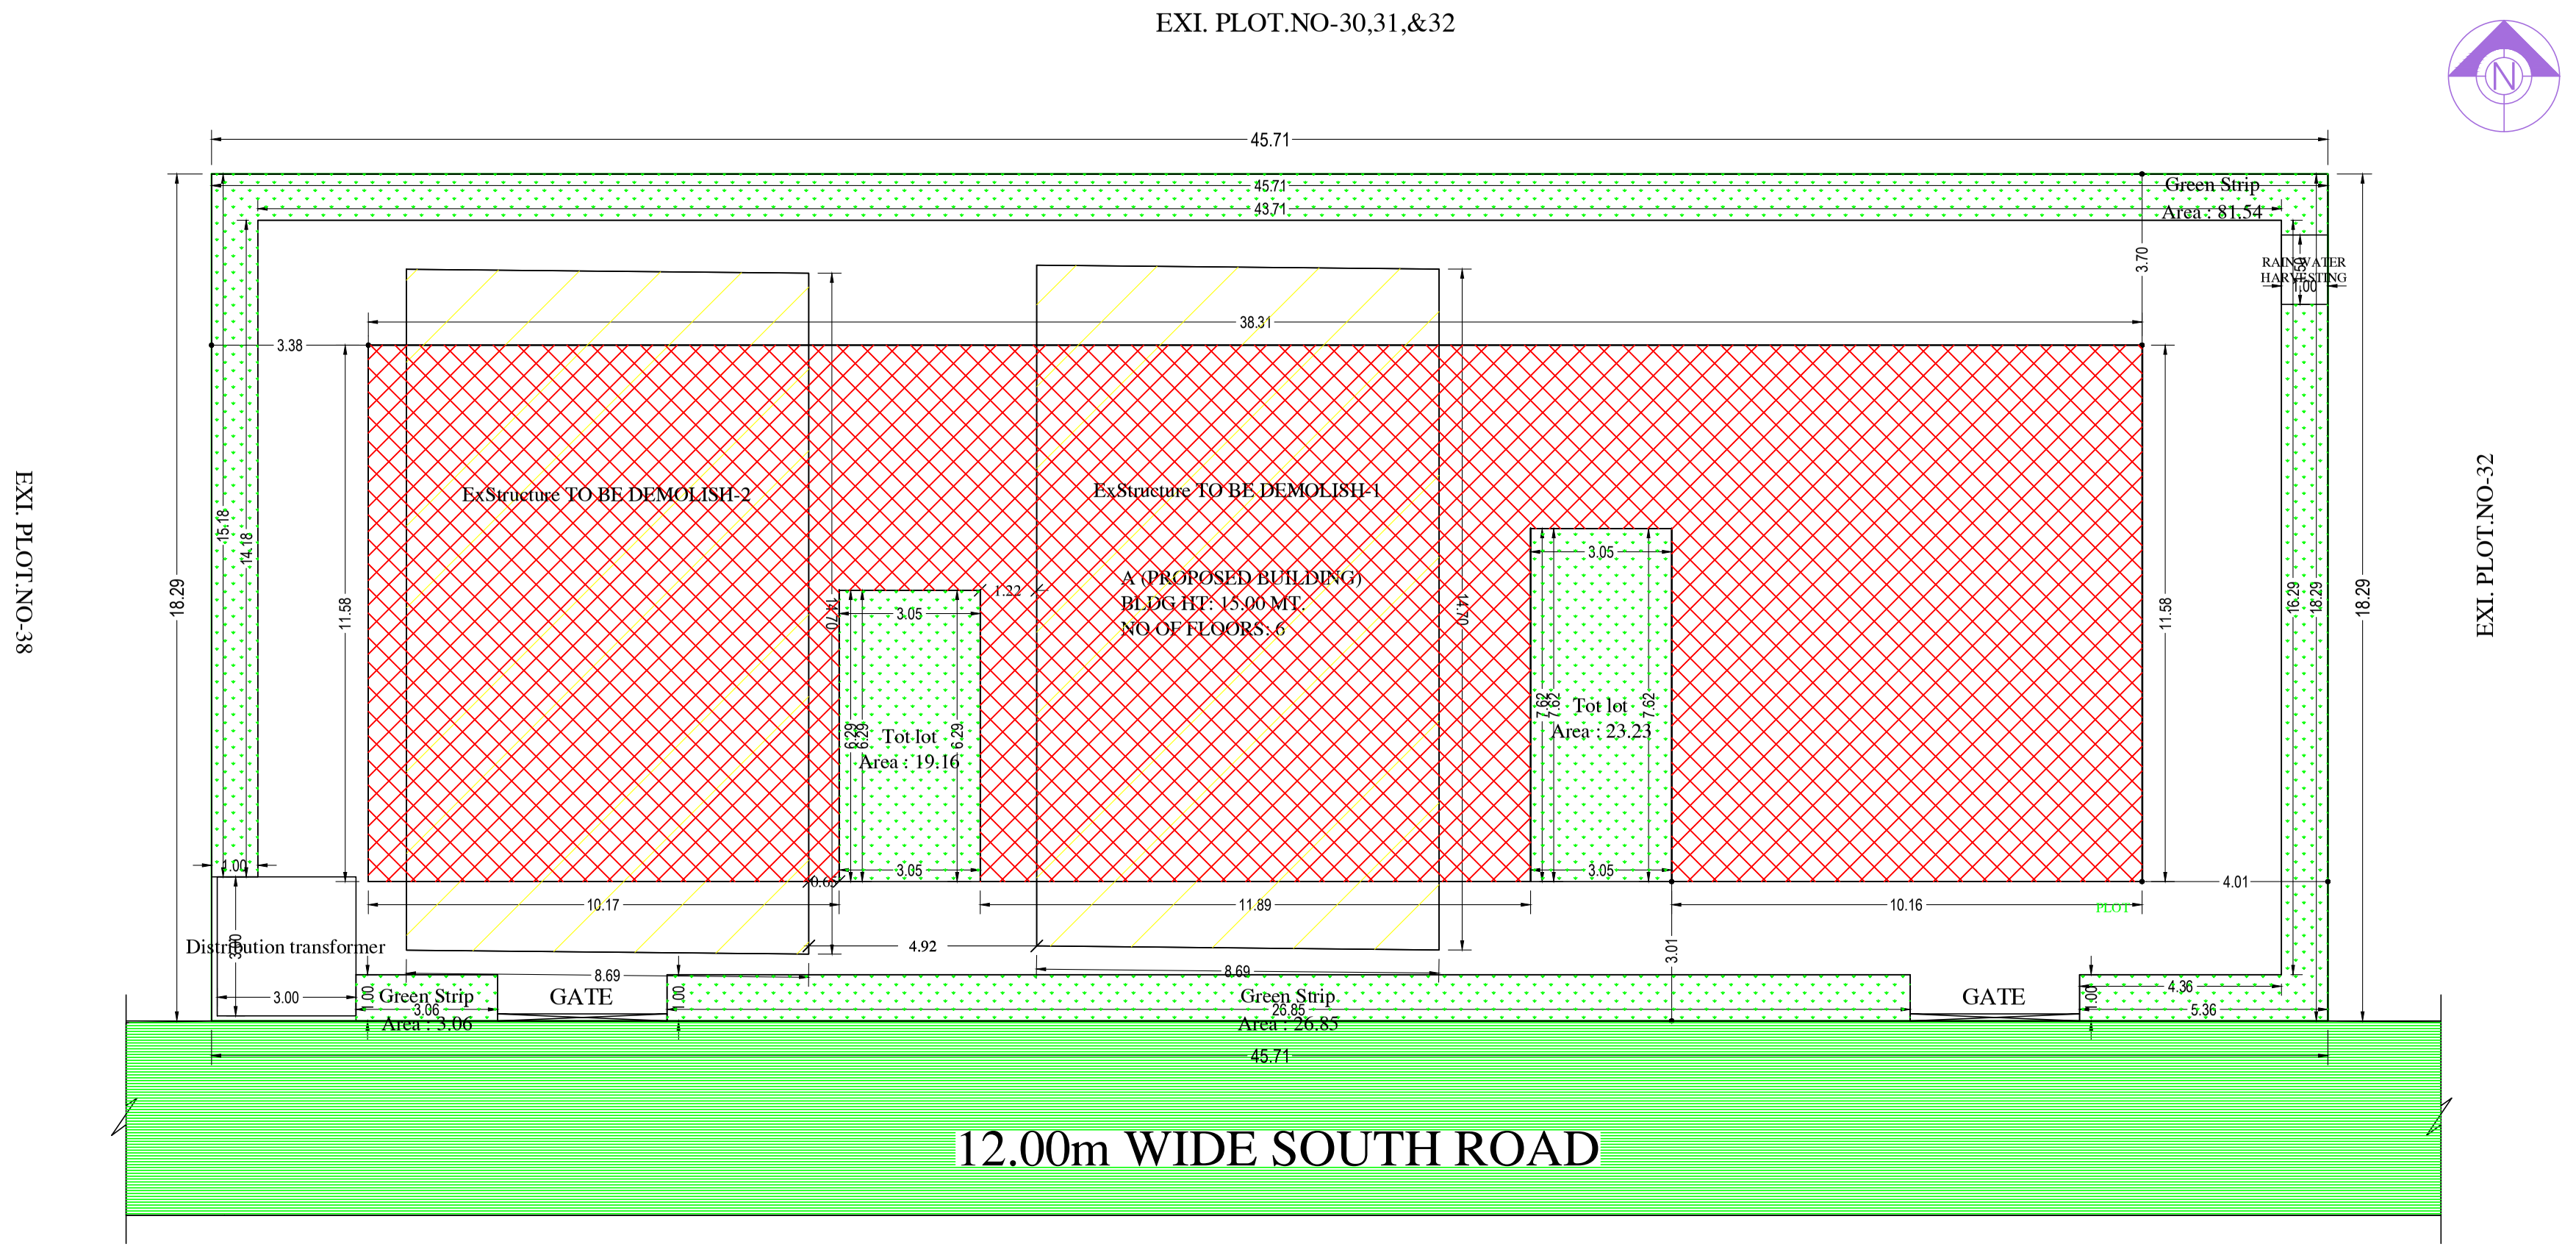

SITE PLAN

	BA NO: 1086/2546/B/Z2/SPG/2024	SHEET NO.	1	DATE	05-07-2024

Project Title :PLAN SHOWING THE PROPOSED CONSTRUCTION OF STILT, GROUND, FIRST, SECOND, THIRD & FOURTHFLOORS R.C.C. ROOF RESIDENTIAL BUILDING BEARING DOOR.NO- 6-116/4 PLOT.NOS-33, 34, 35, 36&37 IN S.NOs-235/1PartAND, 235/2Part OF L.P.NO-1/2002 OF MADHURAWADA VILLAGE SAI PRIYA LAYOUT DIV-4 ZONE-II, G.V.M.C.VISAKHAPATNAM.OWNER'S : M/S. A-SQUARE BUILDERS AND DEVELOPERS, Rep:by.its.Proprietor: Sri.NAGIREDDY SRINIVASA RAO , S/O.N.PRABHAKARA RAO.

AREA STATEMENT	VERSION NO.: 1.101.131 VERSION DATE: 18/06/2024
PROJECT DETAIL:	
Region: VISAKHAPATNAM REGION	Plot Use: Residential
Authority: VISAKHAPATNAM (GVMC)	Plot SubUse: Residential Apartment Bldg
BA No.: 1086/2546/B/Z2/SPG/2024	Land Use Zone: Residential use Zone
Application Type: GeneralProposal	Main Abutting Road Width: 12
Project Type: Building Permission	If Plot is abutting to Highway: No
Nature of Development: Demolition and Reconstruction	Plot No: 33, 34, 35, 36 & 37
Location: MC under VUDA	Survey No.: 235/1part &235/2part
SubLocation: New Areas / Approved Layout Areas	Block No: 1/2002
NatureOfSite: Approved Layout	Premises / Door No.: 33, 34, 35, 36 & 37
Village Name: -	North: PLOT NO - 30, 31&32
Mandal: -	South: ROAD WIDTH - 12.00
Name of Road: SAI PRIYA LAYOUT MADHURAWADA	East: PLOT NO - 32
Ward: Madhurawada Village Ward	West: PLOT NO - 38

AREA DETAILS:		SQ.MT.
AREA OF PLOT (Minimum)	(A)	835.94
NET AREA OF PLOT	(A-Deductions)	835.94
AccessoryUse Area		9.00
Vacant Plot Area		425.59
BUA CHECK		
Residential Net BUA		1996.86
StairCase Area Add in Net BUA		18.53
Net BUA Area		2021.52
Total Net BUA Area		2021.52
BUILT UP AREA CHECK		
Proposed BuiltUp Area		2408.87
Substructure Area Added in Buit up Area		9.00
Total BuiltUp Area		2417.87
Parking Area Check		
Parking Area		SQ.MT.
Required Parking Area		0.00
Proposed Parking Area		390.07

BuildingWise TDR Details

Pwork	Building	Floor	TDR Relaxation Area	TDR Net BUA Area
A-1 (PROPOSED BUILDING)	A (PROPOSED BUILDING)	Ground Floor	18.60	0.00
		First Floor	18.60	0.00
		Second Floor	18.60	0.00
		Third Floor	18.60	0.00
		Fourth Floor	18.60	0.00
Total:			93.00	0.00

LTP NAME AND SIGNATURE	STRUCTURAL ENG NAME AND SIGNATURE	BUILDER NAME AND SIGNATURE
P Narasa Raju		A.Square Builders & Developers
108/2018-19		REG/1086/DEV/0001/2016

Mortgage Area Details

Name	Mortgage Area	
	Reqd	Prop
Built Up Area to Mortgage	199.69	235.45

TDR Details

ID	DRCAREA	DRCOWNER	DRCNO
44439	93.17	-	1060/00223/TDR/DUM/2023
Total	93.17		

Permissible TDR Area

Perm TDR	Prop TDR	Balanced TDR
93.17	93.00	0.17

General Conditions

No.	General Conditions
1	LTP is responsible for any misrepresentation in above aspects.
2	The norms of the staircase, travel distance, width of exit shall be maintained as per NBC.

Building :A (PROPOSED BUILDING)

Floor Name	Total Built Up Area (Sq.mt.)	Proposed Net BUA Area (Sq.mt.)	Total Net BUA Area (Sq.mt.)	Dwelling Units (No.)
		Resi.		
Stilt Floor	401.36	0.00	14.01	00
Ground Floor	399.37	399.37	399.37	03
First Floor	399.37	399.37	399.37	03
Second Floor	399.37	399.37	399.37	03
Third Floor	399.37	399.37	399.37	03
Fourth Floor	399.37	399.37	399.37	03
Terrace Floor	10.66	0.00	10.66	00
Total:	2408.87	1996.85	2021.52	15
Total Number of Same Buildings:	1			
Total:	2408.87	1996.85	2021.52	15

UnitBUA Table for Building :A (PROPOSED BUILDING)

Floor	Name	UnitBUA Type	Gross UnitBUA Area	UnitBUA Area	Deductions (Area in Sq.mt.)		Carpet Area	No. of Rooms	No. of Unit
					Balcony/Verandah	Wall			
TYPICAL - GROUND, FIRST, SECOND& FOURTH FLOOR PLAN	TY F1	FLAT	117.78	117.78	0.00	5.05	112.73	14	3
	TY F2	FLAT	113.91	113.91	4.29	4.41	105.21	14	
	TY F3	FLAT	117.67	117.67	3.70	4.57	109.40	14	
THIRD FLOOR PLAN	3 F1	FLAT	117.78	117.78	0.00	5.05	112.73	14	3
	3 F2	FLAT	113.91	113.91	4.29	4.41	105.21	14	
	3 F3	FLAT	117.67	117.67	3.70	4.57	109.40	14	
Total:	-	-	1746.80	1746.80	39.98	70.14	1636.70	210.00	15.00

Building USE/SUBUSE Details

Building Name	Building Use	Building SubUse	Building Type	Building Structure	Floor Details	Building Fire Group	Type of Roofs
A (PROPOSED BUILDING)	Residential	Residential Apartment Bldg	Single Detached House	Non-Highrise Building	1 Stilt + 1 Ground + 4 upper floors	Group A1	RCC roof

COLOR INDEX	
Plot / Site lines	🟩
Existing street / road	🟩
Proposed work including servicies	🟥
Existing construction proposed to be demolished	🟨
Existing structure to be retained	▨
Work in progress duly sanctioned	🟩
Open Space	☐
Drainage and Sewerage work	🟥
Water Supply work	▨
Deviations	🟥
Recreation ground	🟩

ISO_full_bleed_2A0_(1189.00_x_1682.00_MM)

This is system generated report and does not require any signature.For further confirmation you can access the department website www.apdpms.ap.gov.in with file number.
Accuracy of Scrutiny Report and Drawing is subject to accuracy of end-user provided data, 3rd party software/hardware/services, etc. We are not liable for any damages which may arise from use, or inability to use the Application.